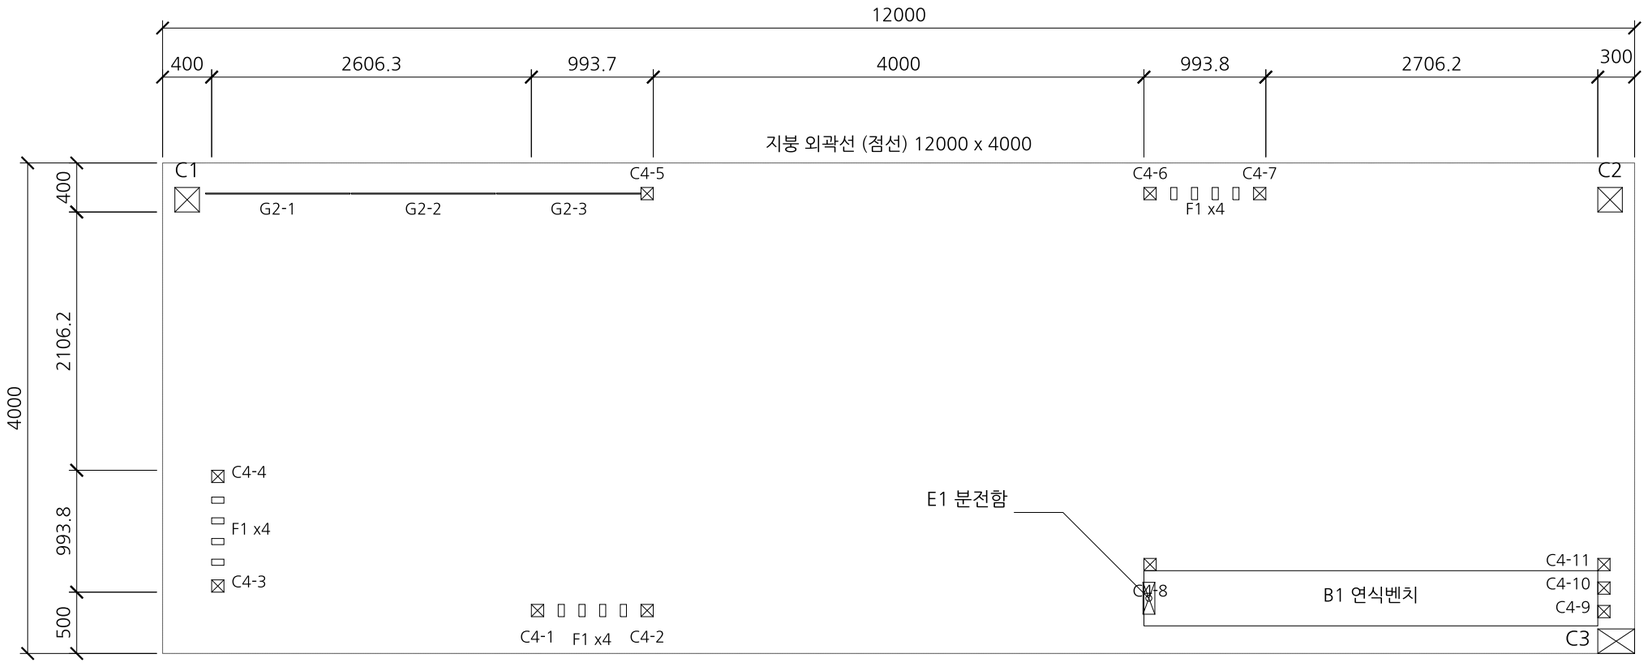




## 기둥·핀·벽체 배치도 (F.L 상부 수평단면)

S = 1/50

※ 비 고


1. 본 배치도는 원도면 '기초평면도'의 앵커(X표기) 위치를 정면도·측면도와 교차 검증하여 작성함.
2. 좌표 원점: 지붕 좌측·전면 모서리 (X=0, Y=0), 높이 기준 F.L ±0.
3. 원도면 기초평면 표기는 지붕 기준 X +50, Y +150 이동 배치되어 있음 (본 도면은 보정치 적용).
4. 각 부품 상세는 PC-01 ~ PC-11 참조. 부품 일람표는 PC-12 참조.

| | |
|---|---|
| 공 사 명 | 조형파고라C(회랑형) 제작 |
| 도 면 명 | 부품 배치도 (KEY PLAN) |
| 부품번호 | - |
| 재　질 | - |
| 수　량 | - |
| 척　도 | 1/50 (A3) |
| 도면번호 | PC-00 |
| 원 도 면 | L-654 조형파고라C |

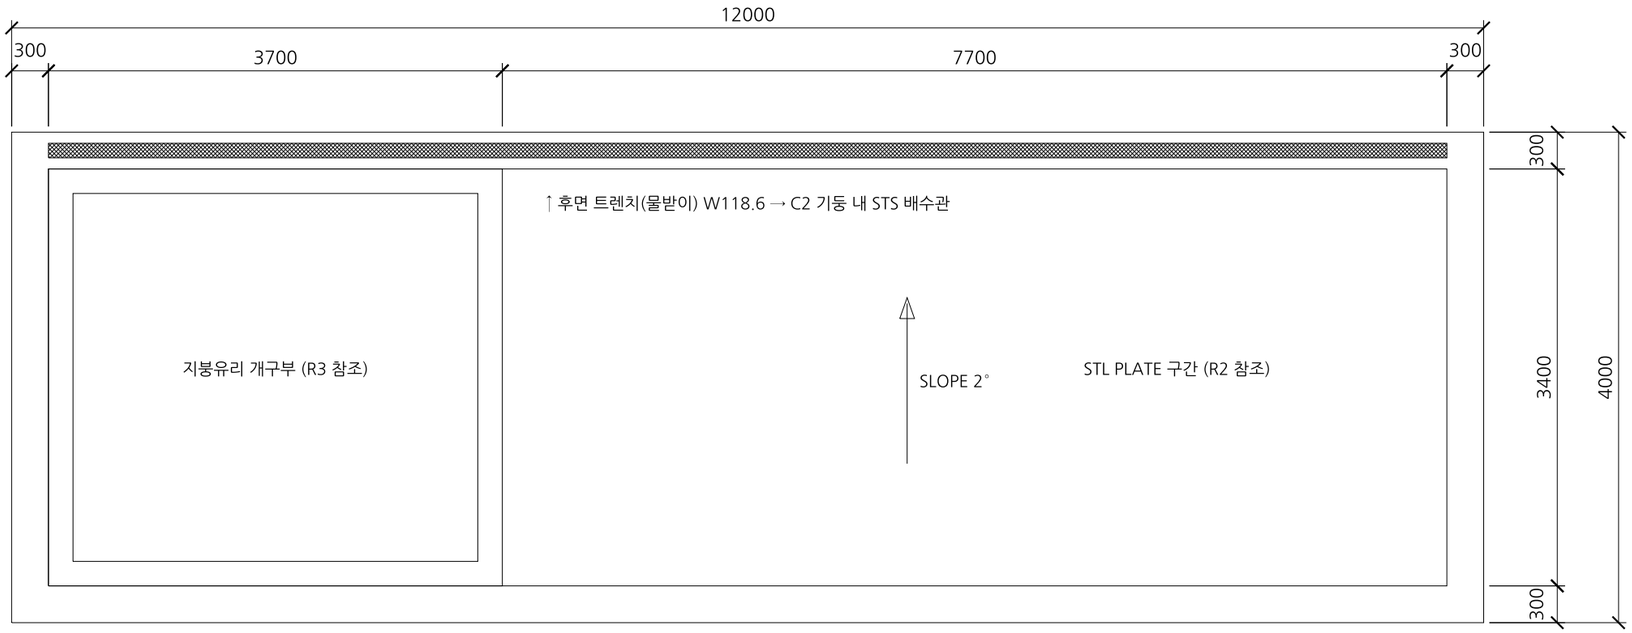



## 지붕 평면도 (상부)

S = 1/50

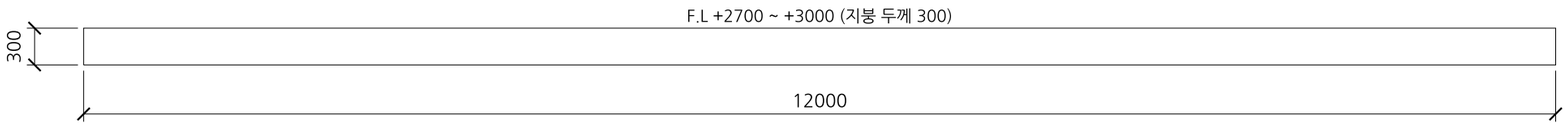


## 정면도

S = 1/50

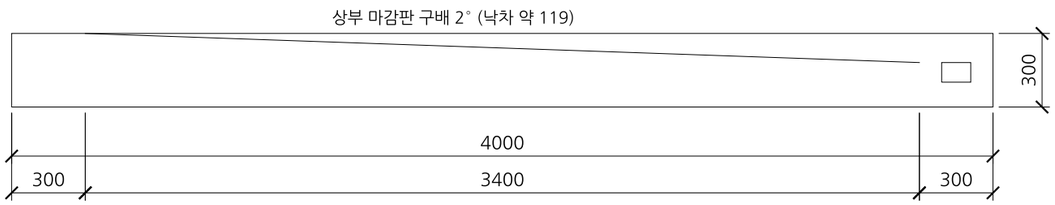



## 측면 단면도 (배수구배)

S = 1/25

※ 비 고


1. 외곽 치수 12000 x 4000, 두께 300 (지붕하부 F.L+2700).
2. 외곽 띠(폭 300) : T1.6 STL PLATE 지정색 도장(삼화페인트 SCN902).
3. 상부 마감면은 후면 방향 2° 구배, 후면 트렌치(W118.6)로 집수.
4. 내부 하지(각관 규격·간격)는 원도면 미표기 → 구조계산 후 확정할 것.
5. 하부: 좌측(X300~4000) 지붕유리 R3, 우측(X4000~11700) 천장판 R2.
6. LED 매입등 8EA 개구부 위치는 PC-02 참조.

| | |
|---|---|
| 공 사 명 | 조형파고라C(회랑형) 제작 |
| 도 면 명 | 지붕 프레임 (R1) |
| 부품번호 | R1 |
| 재　질 | STL 각관 하지 + T1.6 STL PLATE 마감 / 지정색 도장(SCN902) |
| 수　량 | 1 EA |
| 척　도 | 1/50 (A3) |
| 도면번호 | PC-01 |
| 원 도 면 | L-654 조형파고라C |

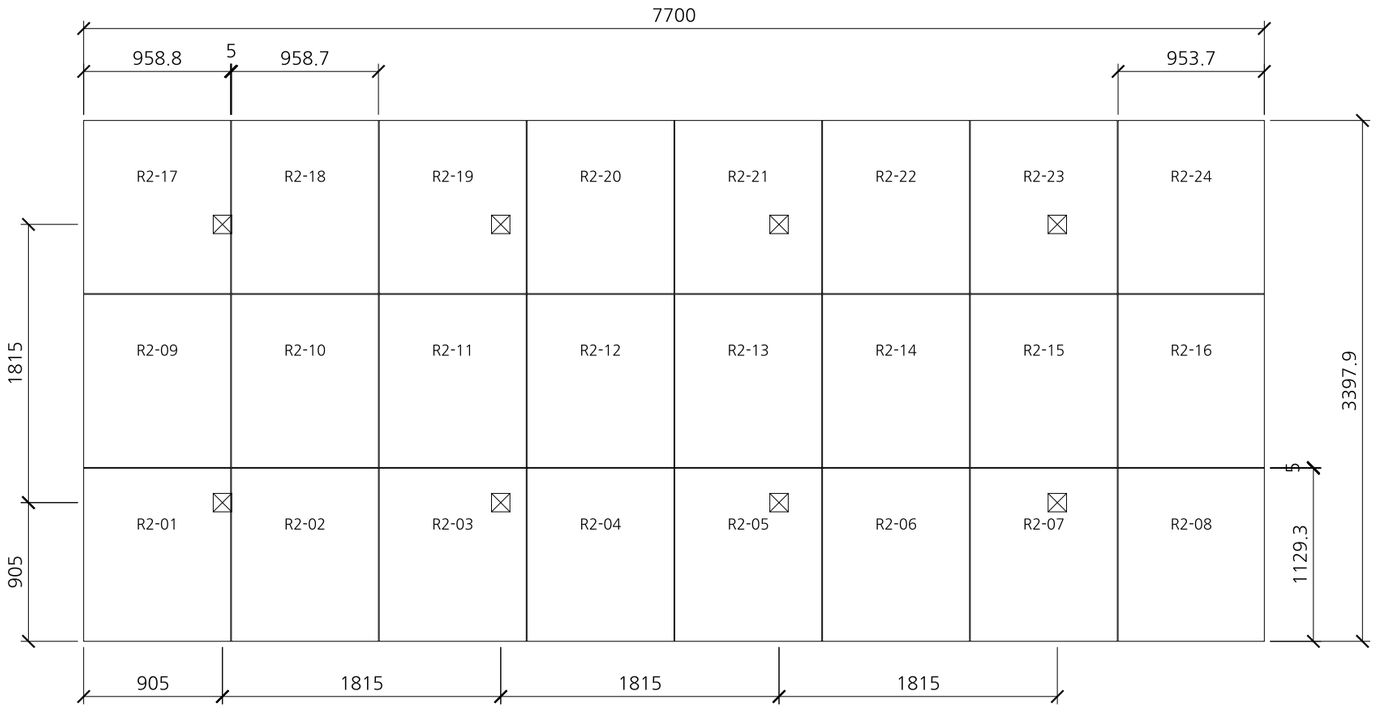


패널 배치도 (지붕 하부에서 올려본 평면)

S = 1/40

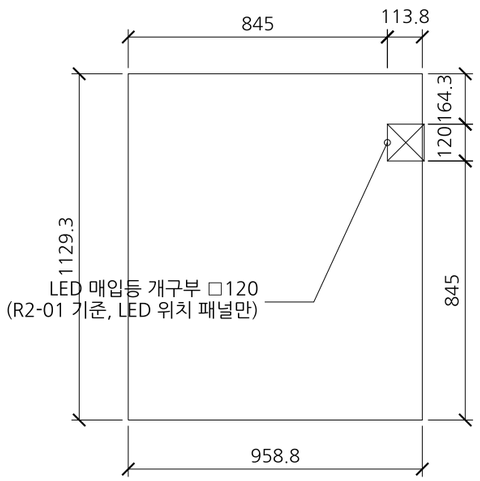


단위 패널 상세 (R2 표준)


S = 1/20

| 구분 | 규격(W x L) | 수량 | 비고 |
|---|---|---|---|
| R2-A | 958.8 x 1129.3 | 21 | 표준 (LED 개구부 6EA 포함) |
| R2-B | 953.7 x 1129.3 | 3 | 우측 끝열 (X10746.3~11700) |
| LED | □120 개구 | 8 | 4열 x 2행, 피치 1815 / 1815 |

※ 비 고

1. T1.6 STL PLATE, 지정색 도장 (삼화페인트 SCN902).
2. 패널 줄눈 5mm (X·Y 공통), 지붕 하부 F.L+2700 면에 부착.
3. 우측 끝열 3EA는 폭 953.7 로 현장 맞춤 재단.
4. 4변 절곡(플랜지) 및 고정 방법은 원도면 미표기 → 제작사 표준 적용.
5. LED 매입등 : 총 8EA, 128W (원도면 기준).
6. LED 개구부 위치는 패널마다 상이 → 배치도 좌표로 타공.

| | |
|---|---|
| 공 사 명 | 조형파고라C(회랑형) 제작 |
| 도 면 명 | 천장 STL PLATE 패널 (R2) |
| 부품번호 | R2 |
| 재　질 | T1.6 STL PLATE / 지정색 도장(SCN902) |
| 수　량 | 24 EA |
| 척　도 | 1/40 (A3) |
| 도면번호 | PC-02 |
| 원 도 면 | L-654 조형파고라C |

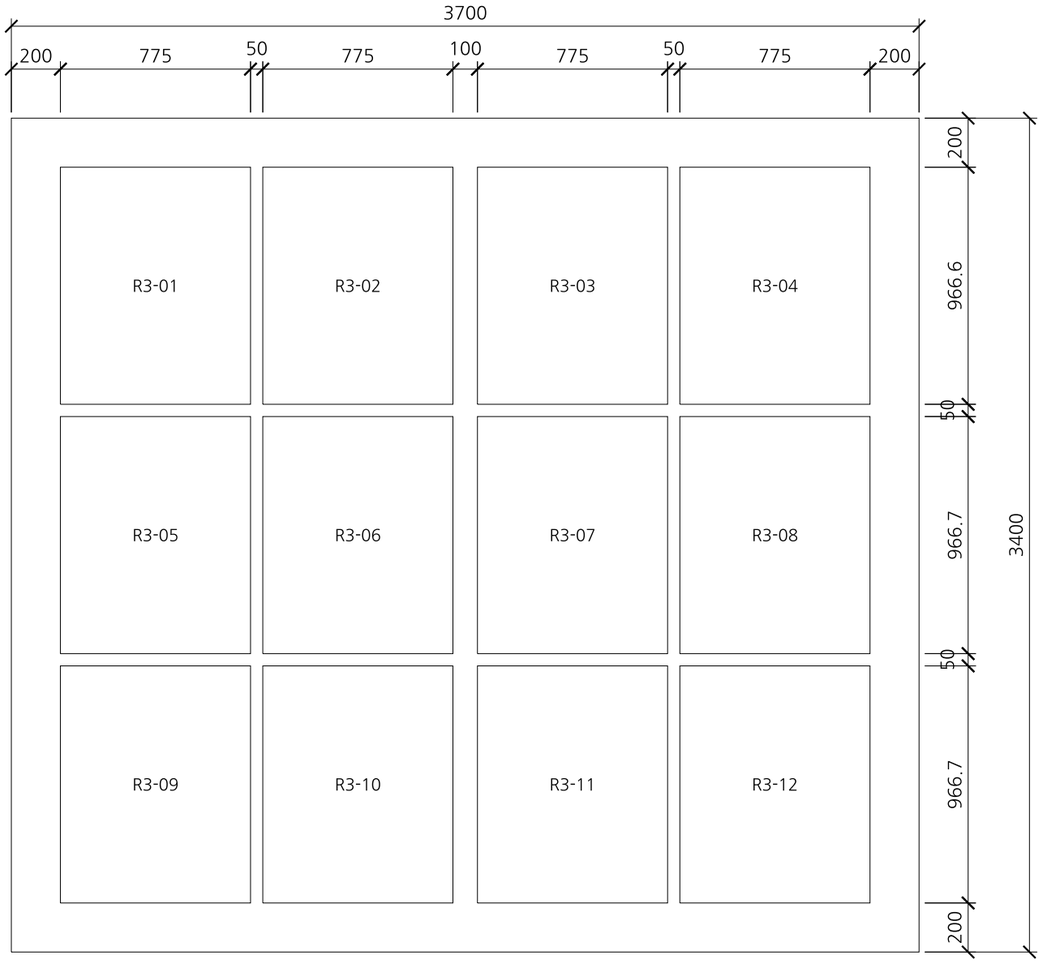



## 지붕유리 배치도 (평면)

S = 1/25


※ 비 고

1. T10.76 KS인증 접합유리 (5 + PVB0.76 + 5), 보호필름 부착.
2. 가시광 투과율 20%.
3. 크기 775 x 966.7, 12EA (4열 x 3행).
4. 줄눈: X방향 50 / 100(중앙) / 50, Y방향 50.
5. 지지 프레임(유리 받침) 상세는 원도면 미표기
   → 실링·세팅블록 포함 제작사 표준 적용.
6. 유리 구성(5+0.76+5)은 T10.76 표준 구성 기준 추정.

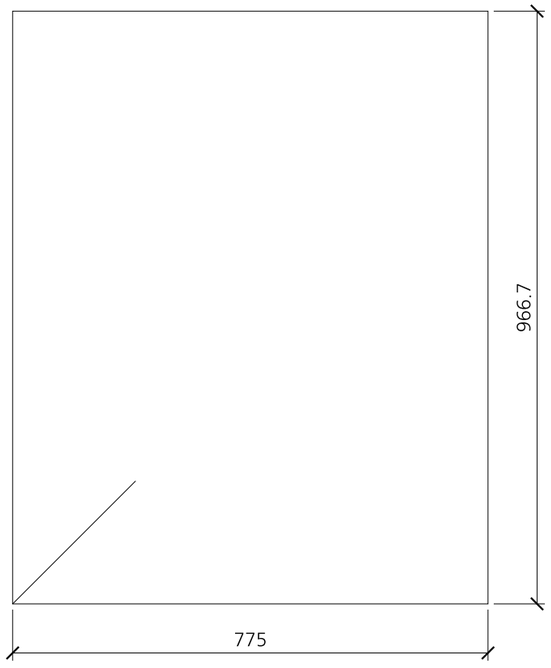


## 단위 유리 상세


S = 1/10

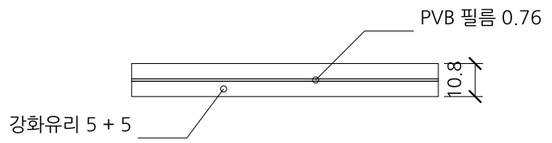


## 유리 단면 (T10.76)

S = 1/2

| | |
|---|---|
| 공 사 명 | 조형파고라C(회랑형) 제작 |
| 도 면 명 | 지붕 접합유리 (R3) |
| 부품번호 | R3 |
| 재　질 | T10.76 KS인증 접합유리 (보호필름/투과율 20%) |
| 수　량 | 12 EA |
| 척　도 | 1/25 (A3) |
| 도면번호 | PC-03 |
| 원 도 면 | L-654 조형파고라C |

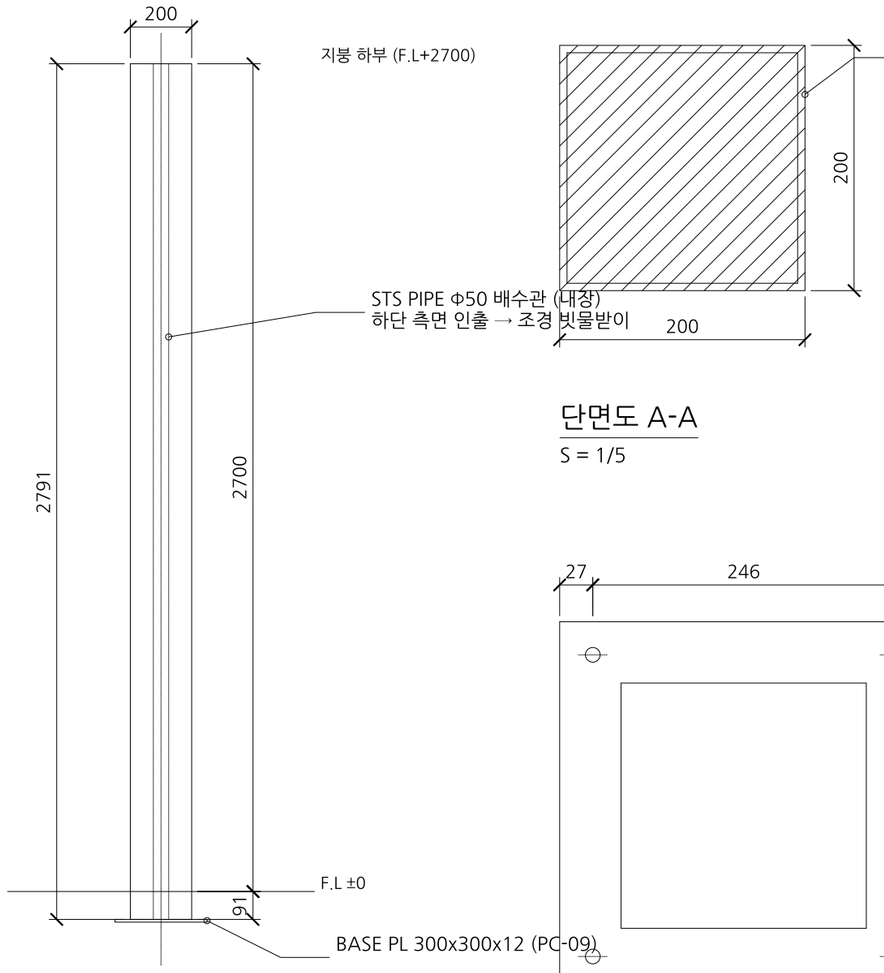



단면도 A-A

S = 1/5

입면도

S = 1/20

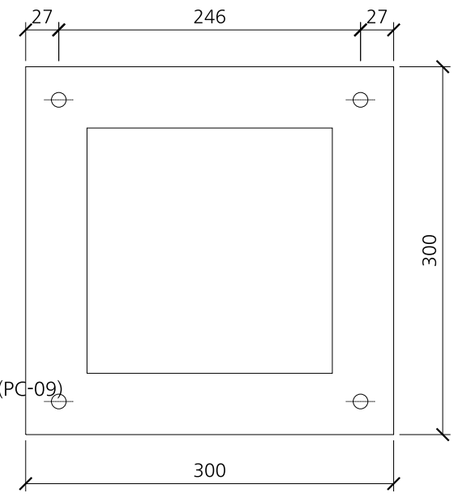


베이스플레이트 평면

S = 1/5

앵커: M10 x L100 셋트앙카 (구멍 Φ12)


설치 위치 (PC-00 좌표, 단위 mm)

| 부호 | X(좌하단) | Y(좌하단) | 단면 |
|---|---|---|---|
| C1 | 100 | 3600 | 200x200 |
| C2 | 11700 | 3600 | 200x200 |

※ 비 고

1. 재질: STL 각관 □200x200 (SS275).
2. 길이 L = 2791 (F.L 상부 2700 + 포장 하부 91).
3. 하단 BASE PLATE 전둘레 용접 후 M10xL100 셋트앙카 고정 (PC-09).
4. 상단은 지붕 하지(R1)에 용접 또는 브라켓 볼트 고정.
5. 수량 2 EA, 표면처리: 지정색 도장 (삼화페인트 SCN902).
6. C2 내부 STS 배수관 내장, 하단 측면 타공


| | |
|---|---|
| 공 사 명 | 조형파고라C(회랑형) 제작 |
| 도 면 명 | □200x200 기둥 (C1/C2) |
| 부품번호 | C1/C2 |
| 재　질 | STL 각관 □200x200 (SS275) |
| 수　량 | 2 EA |
| 척　도 | 1/20 (A3) |
| 도면번호 | PC-04 |
| 원 도 면 | L-654 조형파고라C |

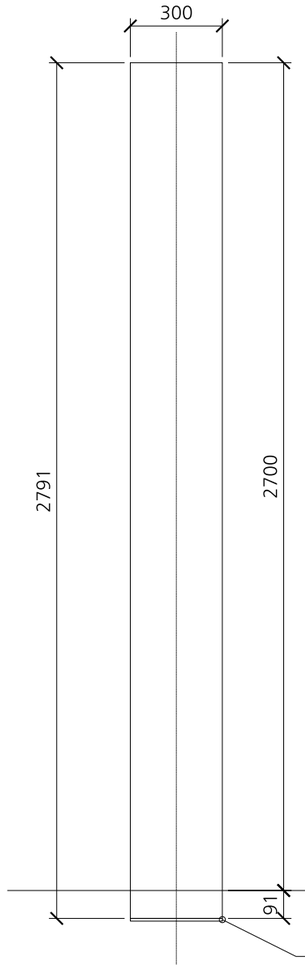


입면도


S = 1/20

지붕 하부 (F.L+2700)

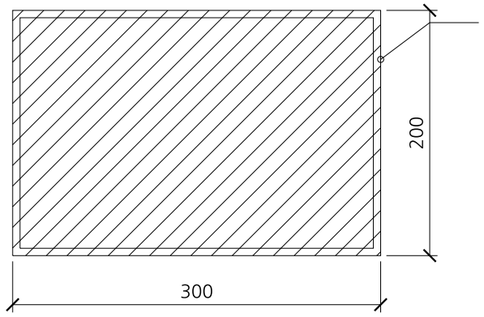


단면도 A-A

S = 1/5

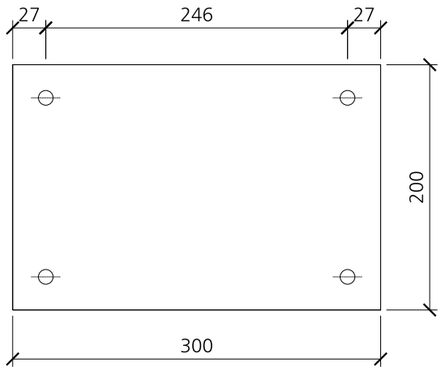


베이스플레이트 평면

S = 1/5

앵커: M10 x L100 셋트앙카 (구멍 Φ12)


설치 위치 (PC-00 좌표, 단위 mm)

| 부호 | X(좌하단) | Y(좌하단) | 단면 |
|---|---|---|---|
| C3 | 11700 | 0 | 300x200 |

※ 비 고


1. 재질: STL 각관 □300x200 (SS275).
2. 길이 L = 2791 (F.L 상부 2700 + 포장 하부 91).
3. 하단 BASE PLATE 전둘레 용접 후 M10xL100 셋트앙카 고정 (PC-09).
4. 상단은 지붕 하지(R1)에 용접 또는 브라켓 볼트 고정.
5. 수량 1 EA, 표면처리: 지정색 도장 (삼화페인트 SCN902).
6. 원도면 기초평면 4모서리 앵커 표기 기준

| | |
|---|---|
| 공 사 명 | 조형파고라C(회랑형) 제작 |
| 도 면 명 | □300x200 기둥 (C3) |
| 부품번호 | C3 |
| 재　질 | STL 각관 □300x200 (SS275) |
| 수　량 | 1 EA |
| 척　도 | 1/20 (A3) |
| 도면번호 | PC-05 |
| 원 도 면 | L-654 조형파고라C |

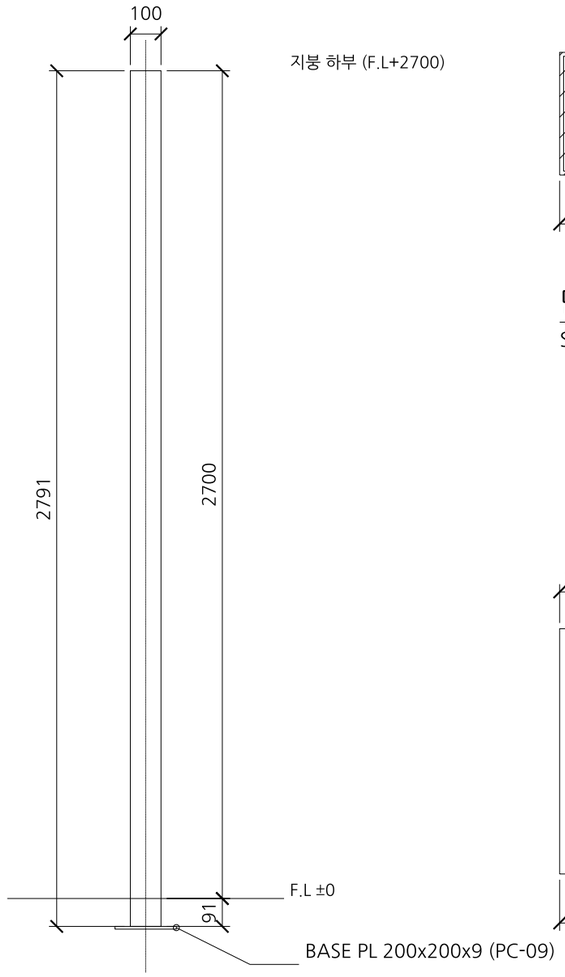



입면도

S = 1/20

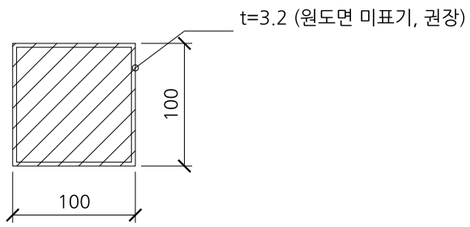


단면도 A-A

S = 1/5

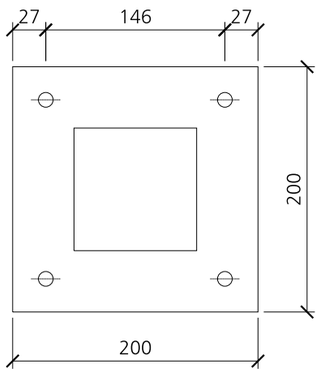


베이스플레이트 평면

S = 1/5

앵커: M10 x L100 셋트앙카 (구멍 Φ12)


설치 위치 (PC-00 좌표, 단위 mm)

| 부호 | X(좌하단) | Y(좌하단) | 단면 |
|---|---|---|---|
| C4-1 | 3006.3 | 300 | 100x100 |
| C4-2 | 3900 | 300 | 100x100 |
| C4-3 | 400 | 500 | 100x100 |
| C4-4 | 400 | 1393.8 | 100x100 |
| C4-5 | 3900 | 3700 | 100x100 |
| C4-6 | 8000 | 3700 | 100x100 |
| C4-7 | 8893.8 | 3700 | 100x100 |
| C4-8 | 8000 | 675 | 100x100 |
| C4-9 | 11700 | 291.7 | 100x100 |
| C4-10 | 11700 | 483.3 | 100x100 |
| C4-11 | 11700 | 675 | 100x100 |

※ 비 고


1. 재질: 100x100 STL PIPE (각관) 지정색 도장.
2. 길이 L = 2791 (F.L 상부 2700 + 포장 하부 91).
3. 하단 BASE PLATE 전둘레 용접 후 M10xL100 셋트앙카 고정 (PC-09).
4. 상단은 지붕 하지(R1)에 용접 또는 브라켓 볼트 고정.
5. 수량 11 EA, 표면처리: 지정색 도장 (삼화페인트 SCN902).

| | |
|---|---|
| 공 사 명 | 조형파고라C(회랑형) 제작 |
| 도 면 명 | □100x100 기둥 (C4) |
| 부품번호 | C4 |
| 재　질 | 100x100 STL PIPE (각관) 지정색 도장 |
| 수　량 | 11 EA |
| 척　도 | 1/20 (A3) |
| 도면번호 | PC-06 |
| 원 도 면 | L-654 조형파고라C |

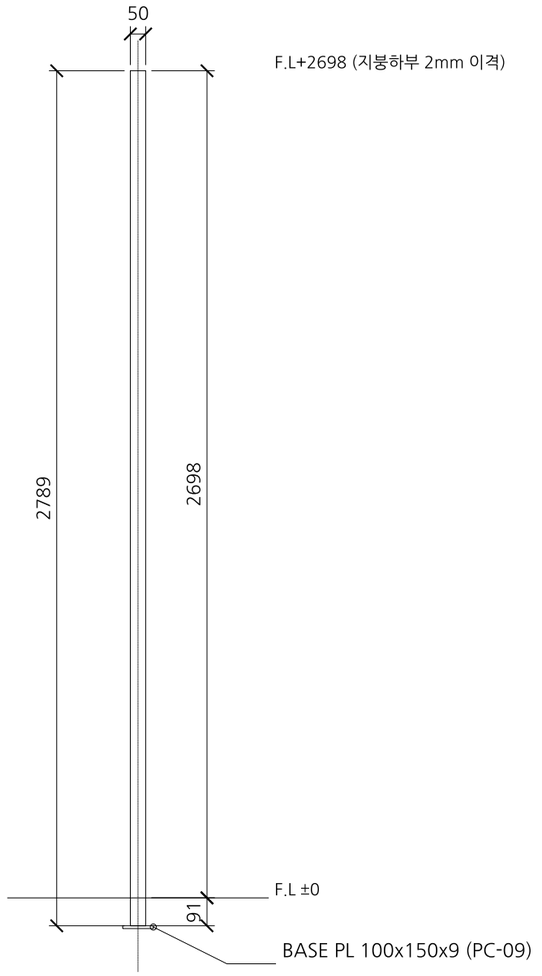



입면도

S = 1/20

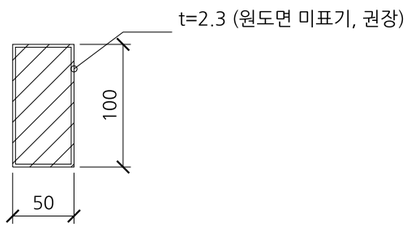


단면도 A-A

S = 1/5

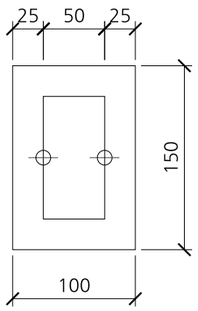


베이스플레이트 평면

S = 1/5

앵커: M10 x L100 셋트앙카 (구멍 Φ12)


설치 위치 (PC-00 좌표, 단위 mm)

| 부호 | X(좌하단) | Y(좌하단) | 단면 |
|---|---|---|---|
| F1-1 | 3225 | 300 | 50x100 |
| F1-2 | 3393.8 | 300 | 50x100 |
| F1-3 | 3562.5 | 300 | 50x100 |
| F1-4 | 3731.3 | 300 | 50x100 |
| F1-5 | 400 | 718.8 | 50x100 |
| F1-6 | 400 | 887.5 | 50x100 |
| F1-7 | 400 | 1056.3 | 50x100 |
| F1-8 | 400 | 1225 | 50x100 |
| F1-9 | 8218.8 | 3700 | 50x100 |
| F1-10 | 8387.5 | 3700 | 50x100 |
| F1-11 | 8556.3 | 3700 | 50x100 |
| F1-12 | 8725 | 3700 | 50x100 |

※ 비 고


1. 재질: 50x100 STL 각관 지정색 도장.
2. 길이 L = 2789 (F.L 상부 2698 + 포장 하부 91).
3. 하단 BASE PLATE 전둘레 용접 후 M10xL100 셋트앙카 고정 (PC-09).
4. 상단은 지붕 하지(R1)에 용접 또는 브라켓 볼트 고정.
5. 수량 12 EA, 표면처리: 지정색 도장 (삼화페인트 SCN902).
6. 핀 피치 168.75 C/C, 지붕하부 2mm 이격

| | |
|---|---|
| 공 사 명 | 조형파고라C(회랑형) 제작 |
| 도 면 명 | 50x100 루버 핀 (F1) |
| 부품번호 | F1 |
| 재　질 | 50x100 STL 각관 지정색 도장 |
| 수　량 | 12 EA |
| 척　도 | 1/20 (A3) |
| 도면번호 | PC-07 |
| 원 도 면 | L-654 조형파고라C |

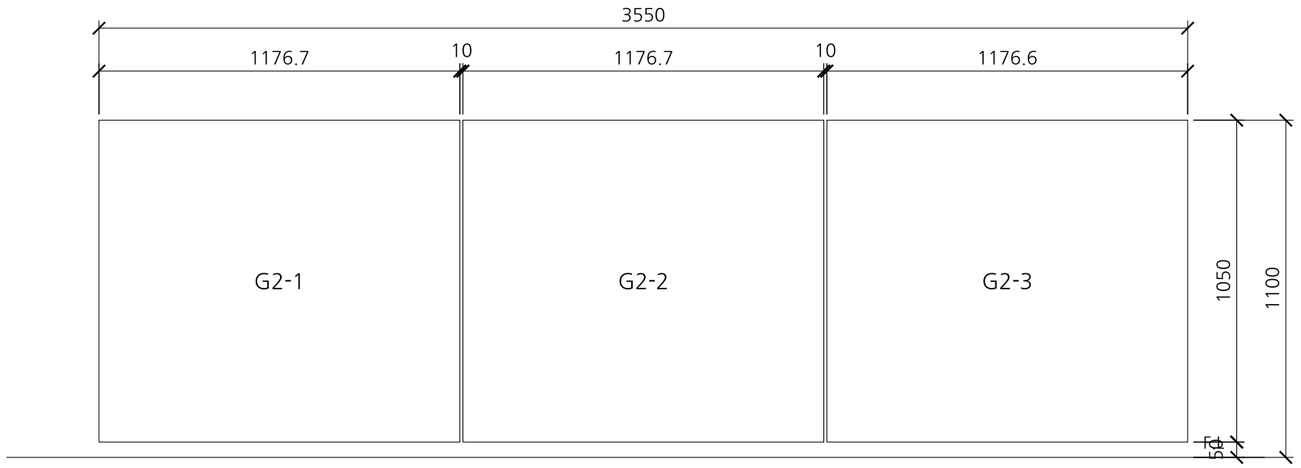


입면도 (후면 좌측 X350~3900)

S = 1/20

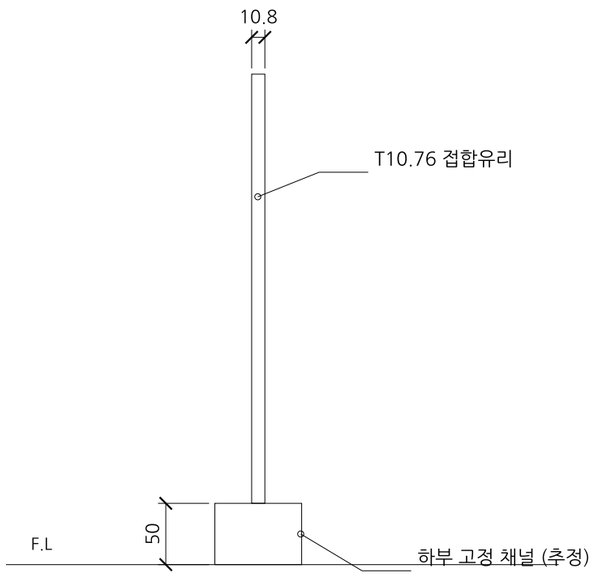



설치 단면 (Y방향)

S = 1/5

※ 비 고


1. T10.76 KS인증 접합유리, 보호필름 부착, 투과율 50%.
2. 크기 1176.7(W) x 1050(H) x 3EA, 유리간 줄눈 10.
3. 설치높이 F.L+50 ~ +1100 (정면도 기준).
4. 설치 위치: 후면 Y3700~3800 라인 (C1 기둥 ~ C4-5 기둥 사이).
5. 고정 방식(채널/클램프)은 원도면 미표기 → 제작사 표준 적용.

| | |
|---|---|
| 공 사 명 | 조형파고라C(회랑형) 제작 |
| 도 면 명 | 벽체 접합유리 (G2) |
| 부품번호 | G2 |
| 재　질 | T10.76 KS인증 접합유리 (보호필름/투과율 50%) |
| 수　량 | 3 EA |
| 척　도 | 1/20 (A3) |
| 도면번호 | PC-08 |
| 원 도 면 | L-654 조형파고라C |

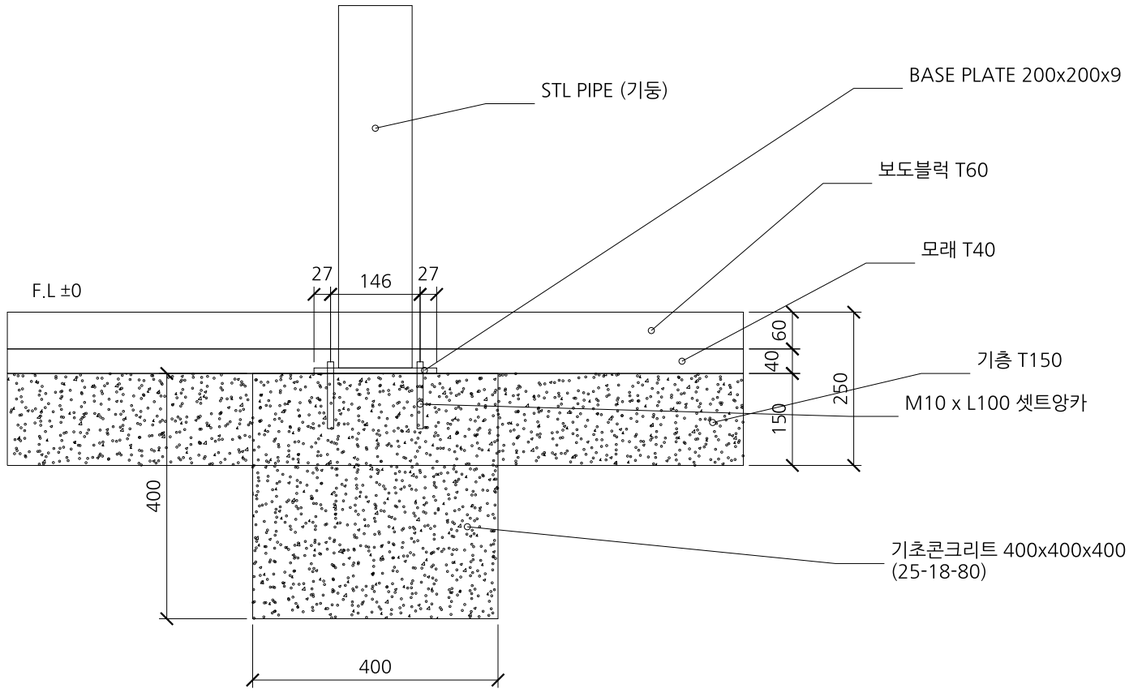


## 기초 단면 상세

S = 1/10

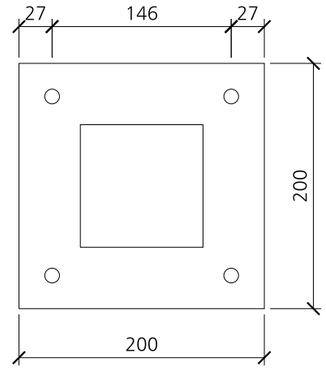


## BASE PLATE 평면 (C4 / □100 기준)


S = 1/5

| 적용 부재 | BASE PL | 앵커 | 수량 |
|---|---|---|---|
| C1/C2 □200 | 300x300x12 | M10 4EA | 2 |
| C3 □300x200 | 300x200x12 | M10 4EA | 1 |
| C4 □100 | 200x200x9 | M10 4EA | 11 |
| F1 50x100 | 100x150x9 | M10 2EA | 12 |

※ 비 고


1. 원도면 상세: BASE PL 200(W) x 9(t) 실측, 앵커 C/C 146, M10xL100 셋트앙카, 기초 400x400x400 (25-18-80).
2. 상기 표 중 □200/□300/핀 BASE PL 규격은 원도면 미표기 → 기둥 단면에 맞춘 제안치 (구조검토 필요).
3. BASE PL 상면 = F.L -91 (포장 하부 매립).
4. 기초 총 26개소 (기둥 14 + 핀 12).

| | |
|---|---|
| 공 사 명 | 조형파고라C(회랑형) 제작 |
| 도 면 명 | 기초 및 BASE PLATE 상세 (FD) |
| 부품번호 | FD |
| 재 질 | 콘크리트 25-18-80 / SS275 |
| 수 량 | 26 EA |
| 척 도 | 1/10 (A3) |
| 도면번호 | PC-09 |
| 원 도 면 | L-654 조형파고라C |

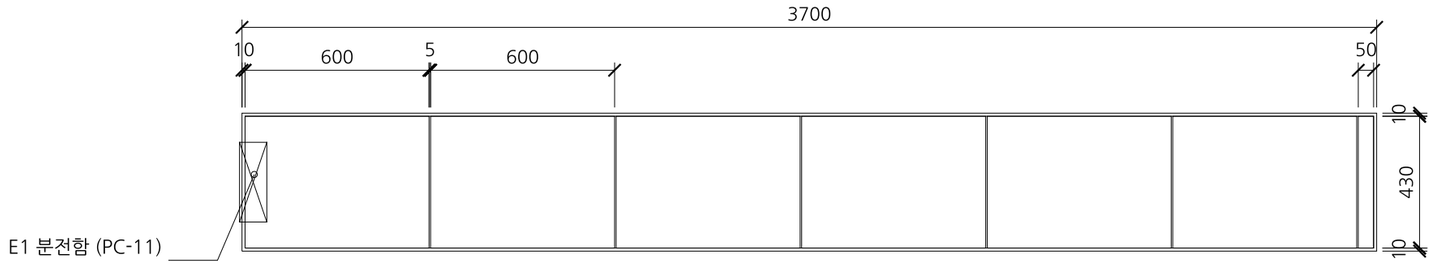



## 평면도

S = 1/20

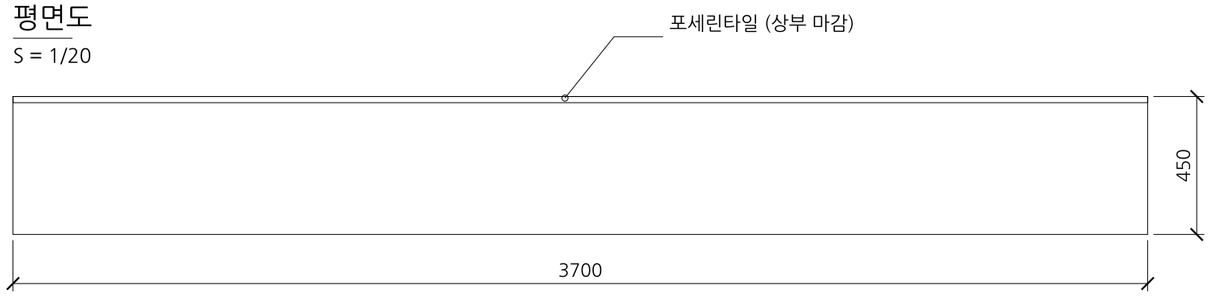


## 정면도

S = 1/20

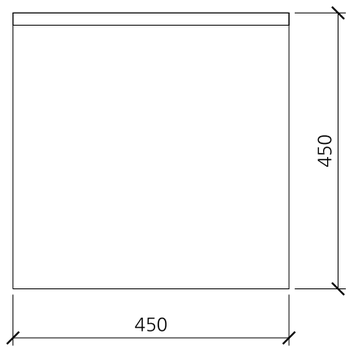



## 측면도

S = 1/10

※ 비 고

1. 설치 위치: X8000~11700, Y225~675 (PC-00).
2. 상판 포세린타일 600 x 430, 줄눈 5, 6EA + 끝단 50 x 430 1EA.
3. 테두리 프레임 폭 10 (평면 기준).
4. 좌측 측면에 분전함(E1) 설치, 하부 배선 F-CV 2.5SQ 이상.
5. 내부 하지 및 타일 접착 방식은 원도면 미표기 → 제작사 표준.
6. 타일 두께는 원도면 미표기 (단면 20 가정).

| | |
|---|---|
| 공 사 명 | 조형파고라C(회랑형) 제작 |
| 도 면 명 | 연식벤치 (B1) |
| 부품번호 | B1 |
| 재　질 | STL 프레임 + (상부) 포세린타일 |
| 수　량 | 1 EA |
| 척　도 | 1/20 (A3) |
| 도면번호 | PC-10 |
| 원 도 면 | L-654 조형파고라C |

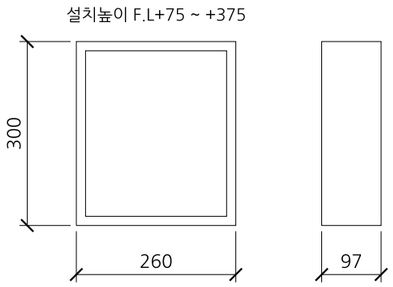



## 분전함 E1 (정면 / 측면)

※ 분전함 사양
- 0.5kW 이상 (220V, 단상)
- 제품 내 모든 전선 2.5SQ 이상 F-CV선
- 누전차단기, 접지 부스바, 타이머 적용
- 1차 전기인입: 전기공사분 / 조경공사분 (원도면)
- 크기는 원도면 축척 실측치 (기성품 선정 시 조정)

※ LED 매입등 L1
- 등기구류: 128W (8EA, 실사용전력은 기구에 따라 다름)
- 총 전기용량: 128 x 1.3(여유율) = 0.5kW
- 배치: X 4905/6720/8535/10350, Y 1205/3020

※ 비 고
1. 지붕 상부 2° 구배 → 후면 트렌치 집수 → C2 기둥 내부 STS 배수관.
2. F.L 하부 약 100 에서 측면 인출, 조경 빗물받이에 연결.
3. 배수관 관경·재질 상세, 집수정 위치는 원도면 '현장협의' 표기.

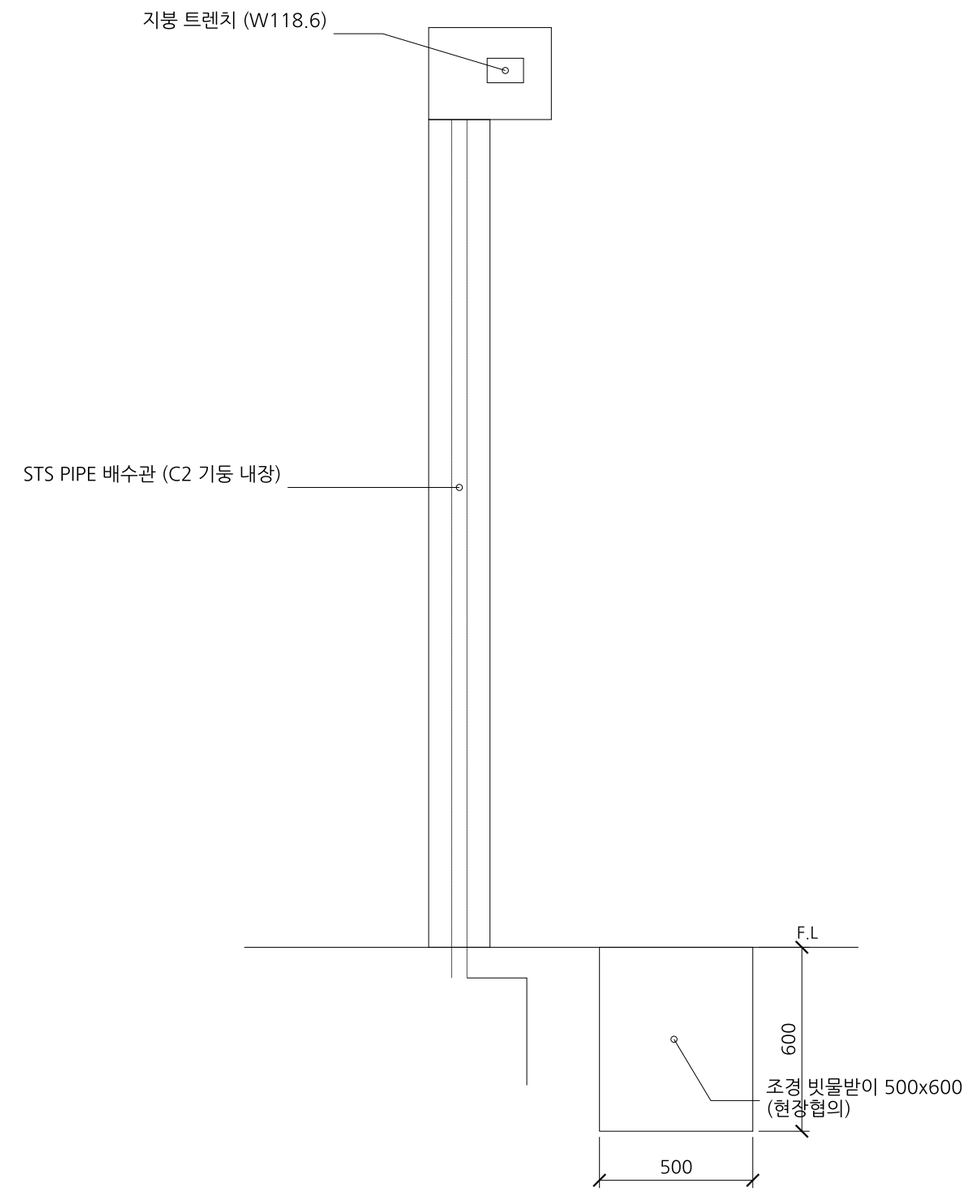


## 배수 계통 (측면, 우측 후면 C2 부근)

S = 1/20

| | |
|---|---|
| 공 사 명 | 조형파고라C(회랑형) 제작 |
| 도 면 명 | 분전함·조명·배수 부속 (E1/L1/D1) |
| 부품번호 | E1/D1 |
| 재 질 | 기성품 + STS304 |
| 수 량 | 1 EA |
| 척 도 | 1/20 (A3) |
| 도면번호 | PC-11 |
| 원 도 면 | L-654 조형파고라C |

| 부호 | 품명 | 규격 | 재질 | 수량 | 단위길이 | 비고 |
|---|---|---|---|---|---|---|
| R1 | 지붕 프레임(외곽 박스) | 12000 x 4000 x H300 | STL 각관 하지 + T1.6 STL PLATE 마감 / 지정색 도장(SCN902) | 1 | - | 내부 하지 구조 원도면 미표기 |
| R2 | 천장 STL PLATE 패널 | 958.8 x 1129.3 (21EA) / 953.7 x 1129.3 (3EA) | T1.6 STL PLATE / 지정색 도장(SCN902) | 24 | - | 줄눈 5mm, LED 개구부 포함 8EA |
| R3 | 지붕 접합유리 | 775 x 966.7 | T10.76 KS인증 접합유리 (보호필름/투과율 20%) | 12 | - | 유리 줄눈 50/100 |
| C1/C2 | □200x200 기둥 | □200x200 L=2791 | STL 각관 □200x200 (SS275) | 2 | 2791.0 | C2 내부 STS 배수관 내장, 하단 측면 타공 |
| C3 | □300x200 기둥 | □300x200 L=2791 | STL 각관 □300x200 (SS275) | 1 | 2791.0 | 원도면 기초평면 4모서리 앵커 표기 기준 |
| C4 | □100x100 기둥 | □100x100 L=2791 | 100x100 STL PIPE (각관) 지정색 도장 | 11 | 2791.0 |  |
| F1 | 50x100 루버 핀 | □50x100 L=2789 | 50x100 STL 각관 지정색 도장 | 12 | 2789.0 | 핀 피치 168.75 C/C, 지붕하부 2mm 이격 |
| G2 | 벽체 접합유리 | 1176.7 x 1050 | T10.76 KS인증 접합유리 (보호필름/투과율 50%) | 3 | - | 후면 좌측 벽 |
| FD | 기둥 기초 + BASE PLATE | 기초 400x400x400 / BASE PL 200x200x9 | 콘크리트 25-18-80 / SS275 | 26 | - | 기둥·핀 1개소당 1EA |
| B1 | 연식벤치 | 3700 x 450 x H450 | STL 프레임 + (상부) 포세린타일 | 1 | 3700 | 타일 600x430 x6 + 50x430 x1 |
| E1/D1 | 분전함·조명·배수 부속 | 분전함 260x300x97 / LED 8EA / STS 배수관 | 기성품 + STS304 | 1 | - |  |
| L1 | LED 매입등 | □120, 16W급 x 8EA = 128W | 기성품 | 8 | - | 지붕 하부 R2 패널 개구부 |
| D1 | STS 배수관 | STS PIPE (Φ50 권장) | STS304 | 1 | 약 3,300 | 트렌치 → C2 내부 → 빗물받이 (현장협의) |
| D2 | 조경 빗물받이 | 500 x 600 (집수정) | 기성품 | 1 | - | 현장협의 |

※ 비 고

1. 원도면에 명시된 값: 외곽 치수, 기둥·핀 위치, 유리 규격(T10.76), 강판(T1.6), 기초(400x400x400), 앵커(M10xL100), 도장색(SCN902).
2. 원도면 미표기 → 제안치/추정치(각 도면에 '미표기' 표시): 각관 두께, □200·□300·핀용 BASE PL, 지붕 내부 하지, 유리 지지 프레임.
3. 제작 전 구조계산 및 감리 승인 후 확정할 것.

| | |
|---|---|
| 공 사 명 | 조형파고라C(회랑형) 제작 |
| 도 면 명 | 부품 일람표 (BOM) |
| 부품번호 | - |
| 재　질 | - |
| 수　량 | - |
| 척　도 | 1/1 (A3) |
| 도면번호 | PC-12 |
| 원 도 면 | L-654 조형파고라C |